


Stad och verksamhet

Stadsplanering och hotell vid kajkant vid Göta älv i Göteborg.

Metod: AutoCAD, Indesign, Rhinoceros, V-ray, Photoshop

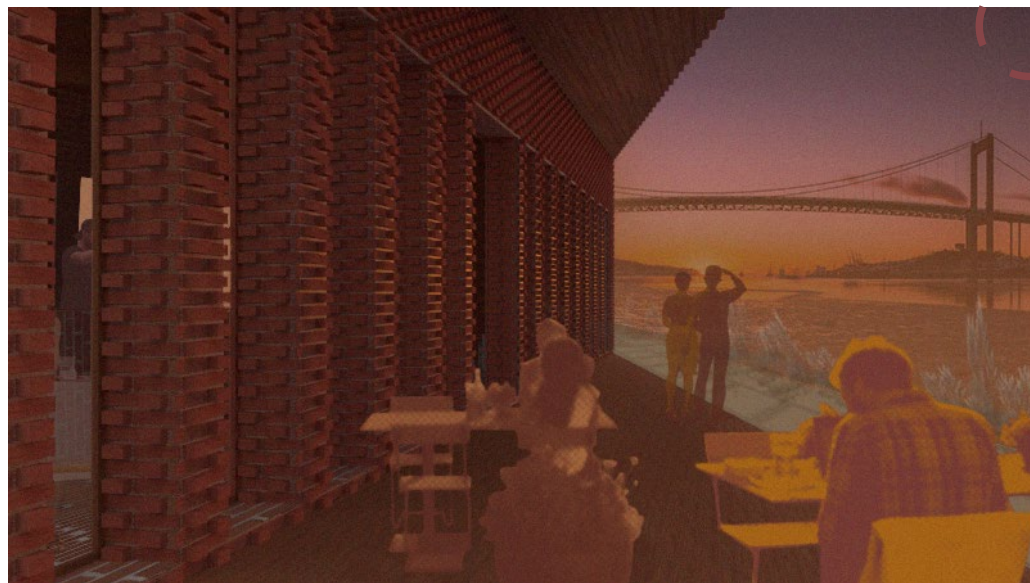

UTESERVERING Restaurangen i Hotell Stella har ett indrag som skapar ett vindstilla gaturum med utsikt över Älvsborgsbron.




GATURUM Utblick mot Eriksbergskranen på andra sidan älven sett från Knallens huvudgata.

Hotell Stella i den nya stadsdelen Knallen


Majnabbekhamnen omvandlas från färjeterminal till en blandad stadsdel med bostäder och verksamheter. Som en del av området tillkommer Hotell Stella vid kajkanten, med restaurang i entréplan och nära koppling till färjeläget Klippan.

Stadsplanen bygger på ett varierat gatunät där gator och volymer möts i olika vinklar, vilket skapar vindstilla nischer för vistelse och stadsliv trots starka havsvindar. Samtidigt ramas utblickar in mot Göteborgstypiska landmärken som Eriksbergskranen och Älvsborgsbron, vilket stärker orienterbarheten och platsens identitet.




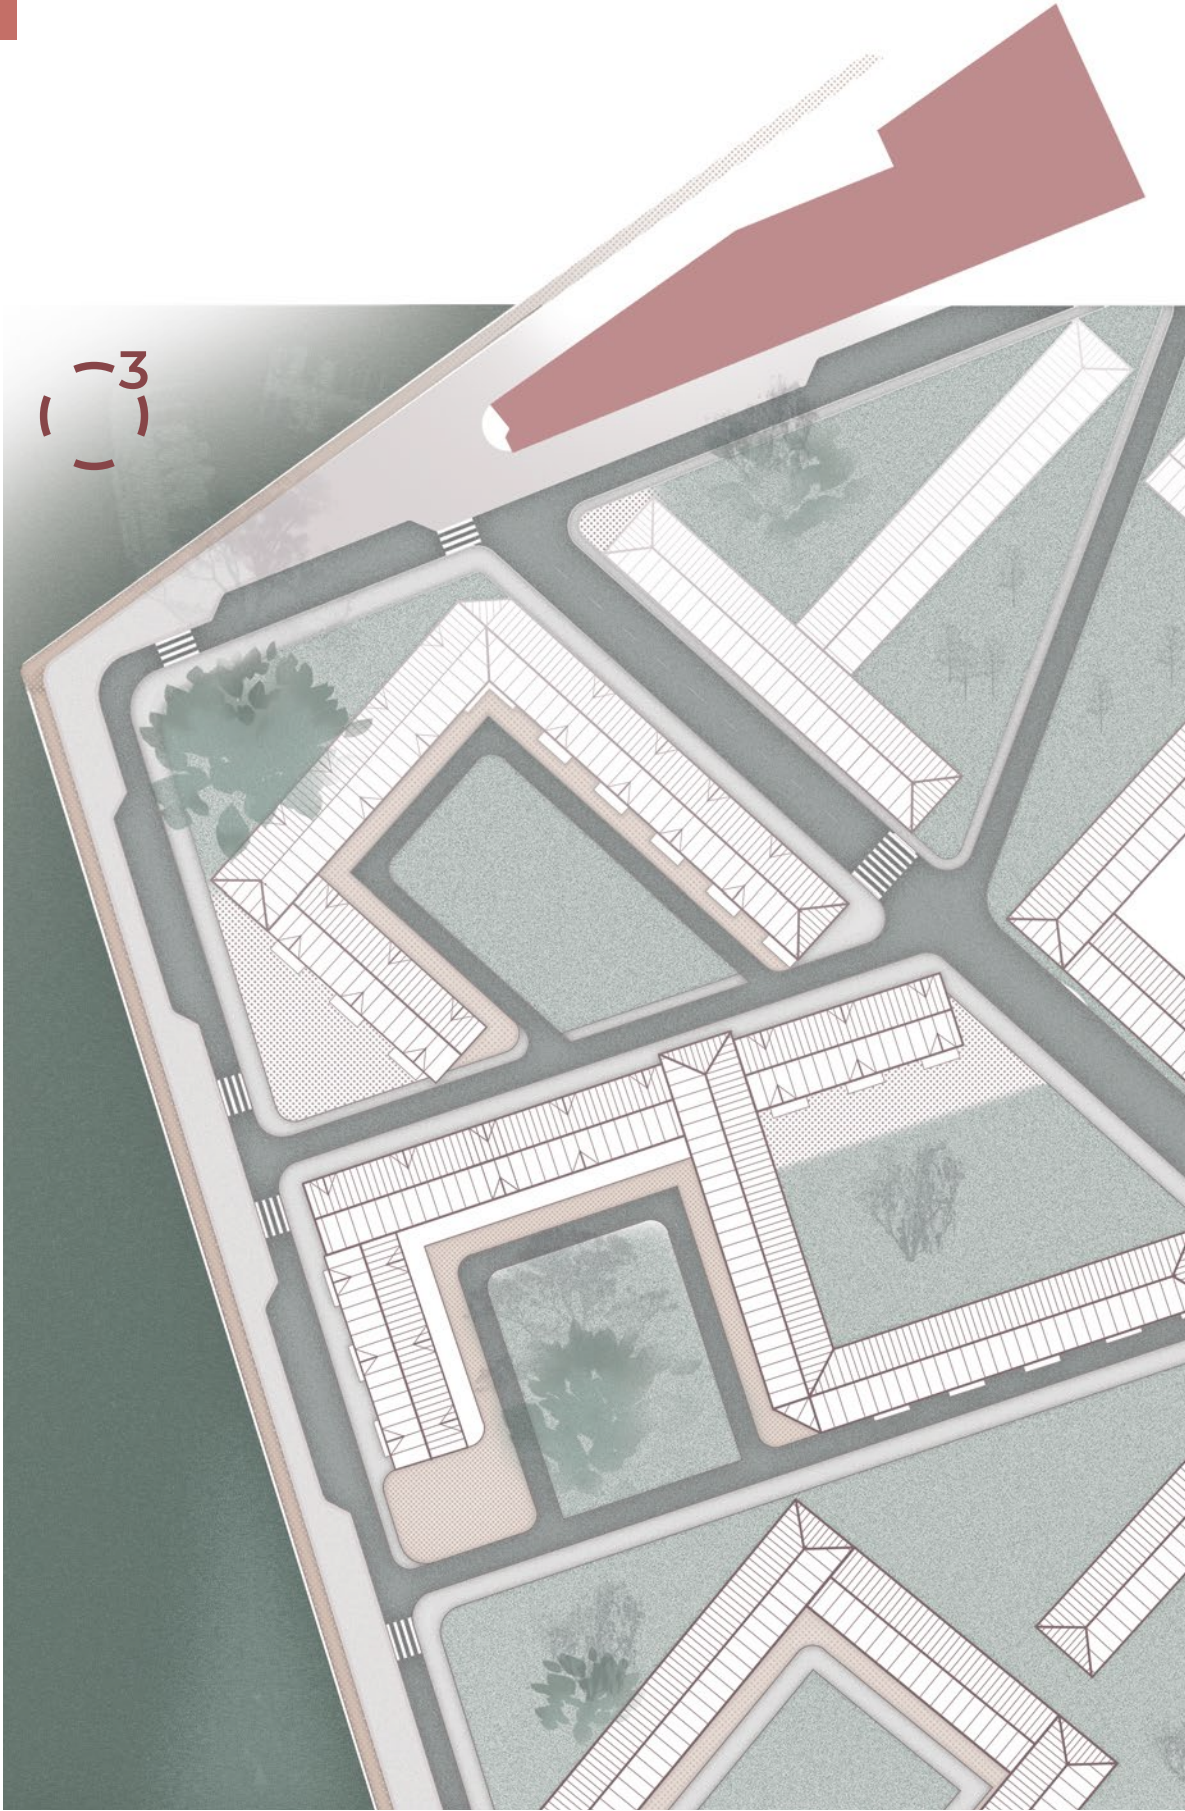

PLANUTSNITT 1:1000 (A1)
Planutsnittet visar taklandskapet och stadsplanens fickor med rumsskapande potential för uteserveringar och pocket parks för allmänheten.

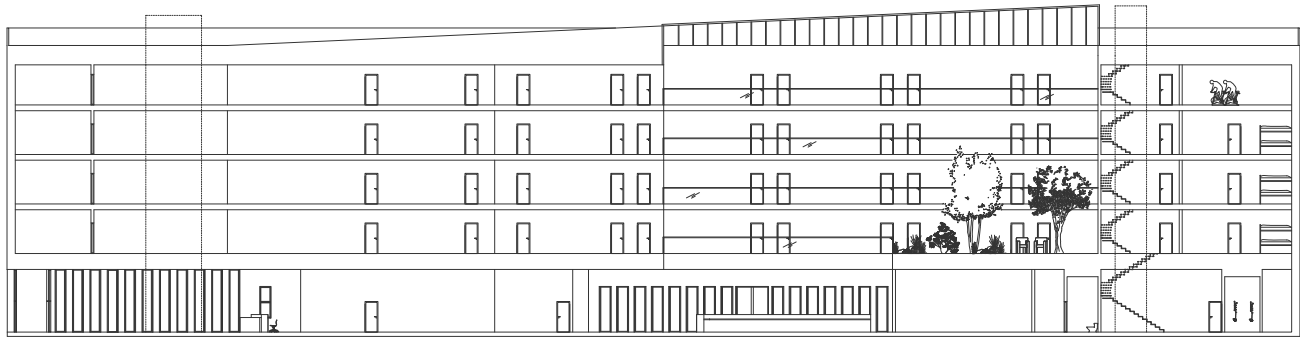



SEKTION B-B 1:200 (A1) Centralt i byggnaden finns ett stort atrium som ger ljus till rumsvåningarnas korridorer och restaurangens bar. På första våningen finns en vinterträdgård som har en visuell förbindelse med restaurangen på bottenplan.

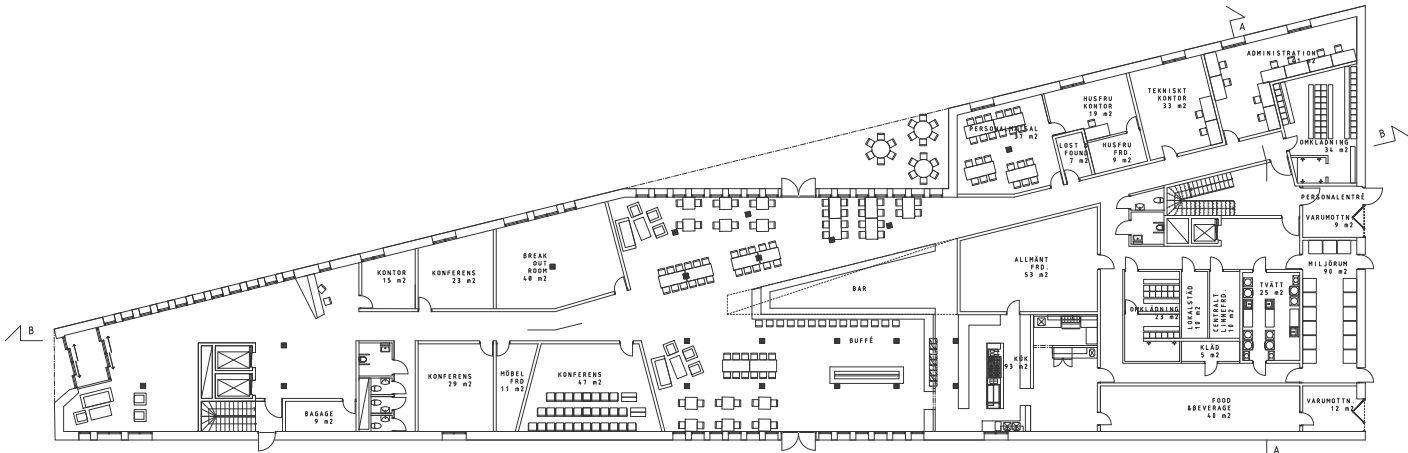


ENTREPLAN 1:200 (A1) Bottenplan är ett offentligt rum och back of house med krav yta för uppehåll och filer för rörelse som måste vara både nära och segregerade från varandra för att fungera.



PERSPEKTIV 3
Vy från färja vid anläggning vid färjeläget Knallen.

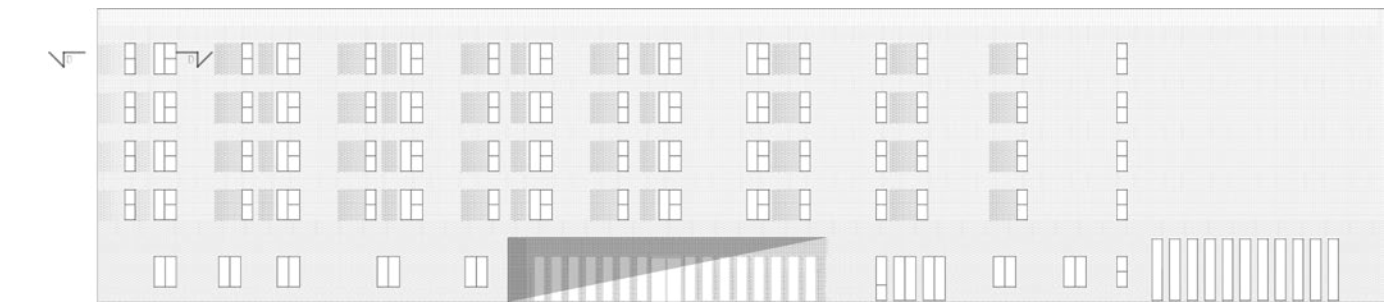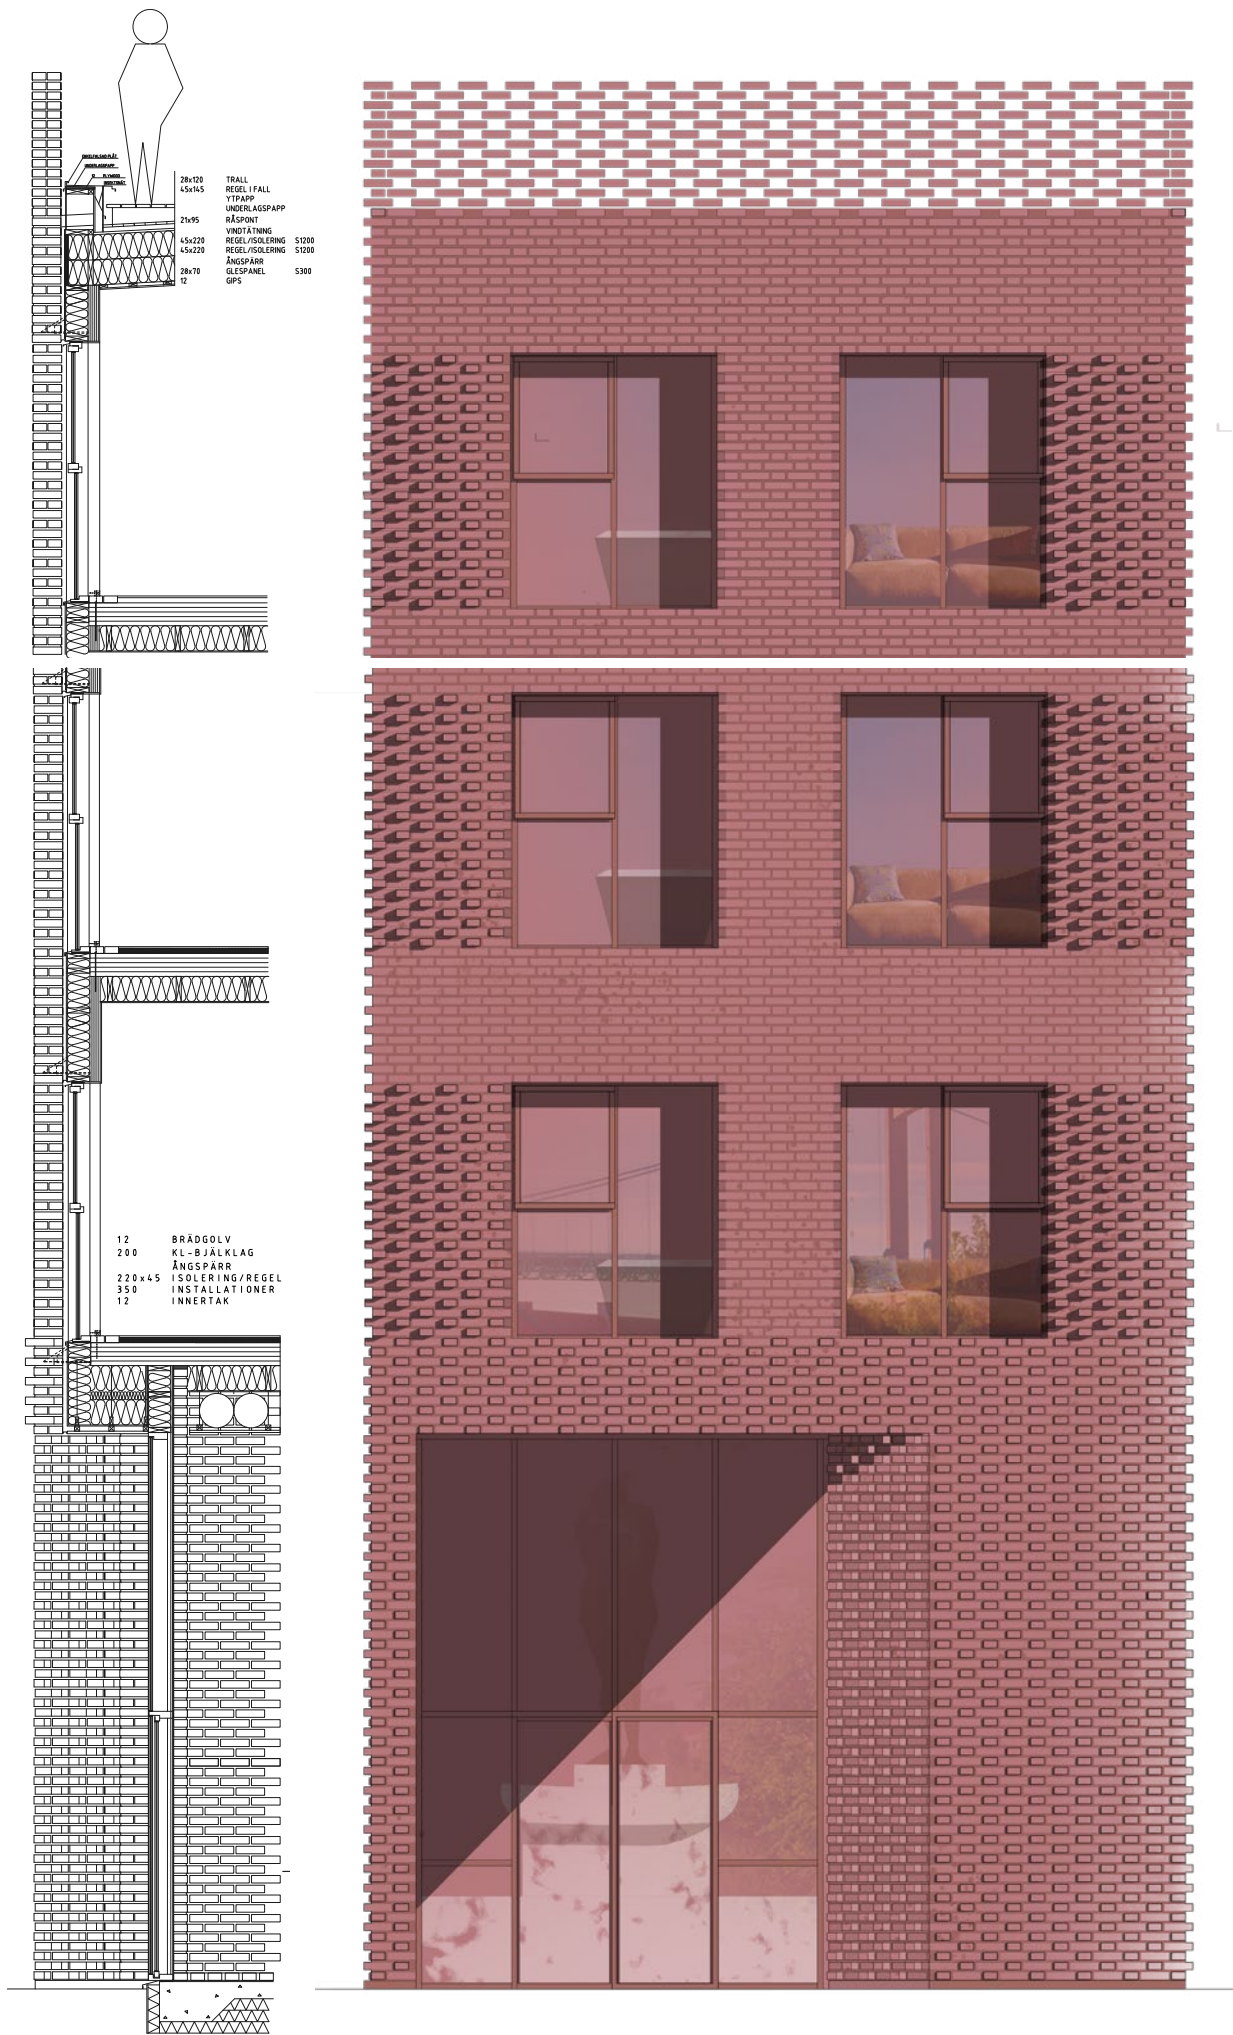

FASAD MOT NORDVAST 1:200 (A1)

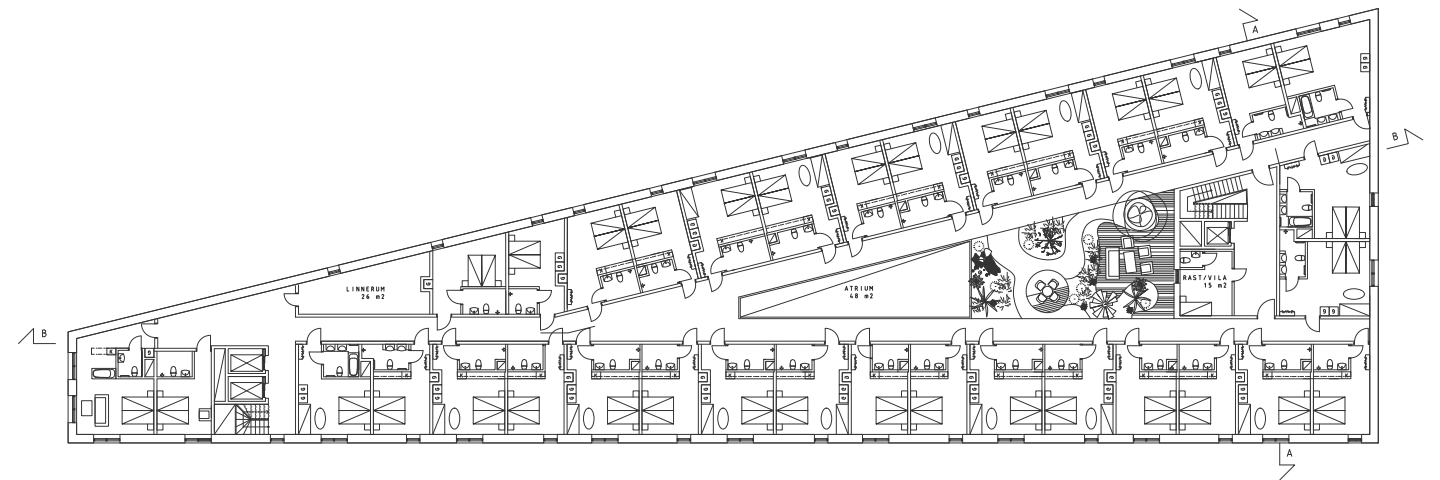

PLAN 1-4 1:200 (A1) *Suiter placerats i byggnadens spets med utsikt mot Älvsborgsbron, rymliga handikappersrum i hörnen och en ett vilrum för städpersonal i den bredaste delen intill atriumet.*



ENTRE/LOBBY *Den ljusa markstenen från torget utanför följer med in. Rakt fram finns receptionsdisken och vid sidan av rörelsen ett rum som kan användas till arbete eller väntan.*